


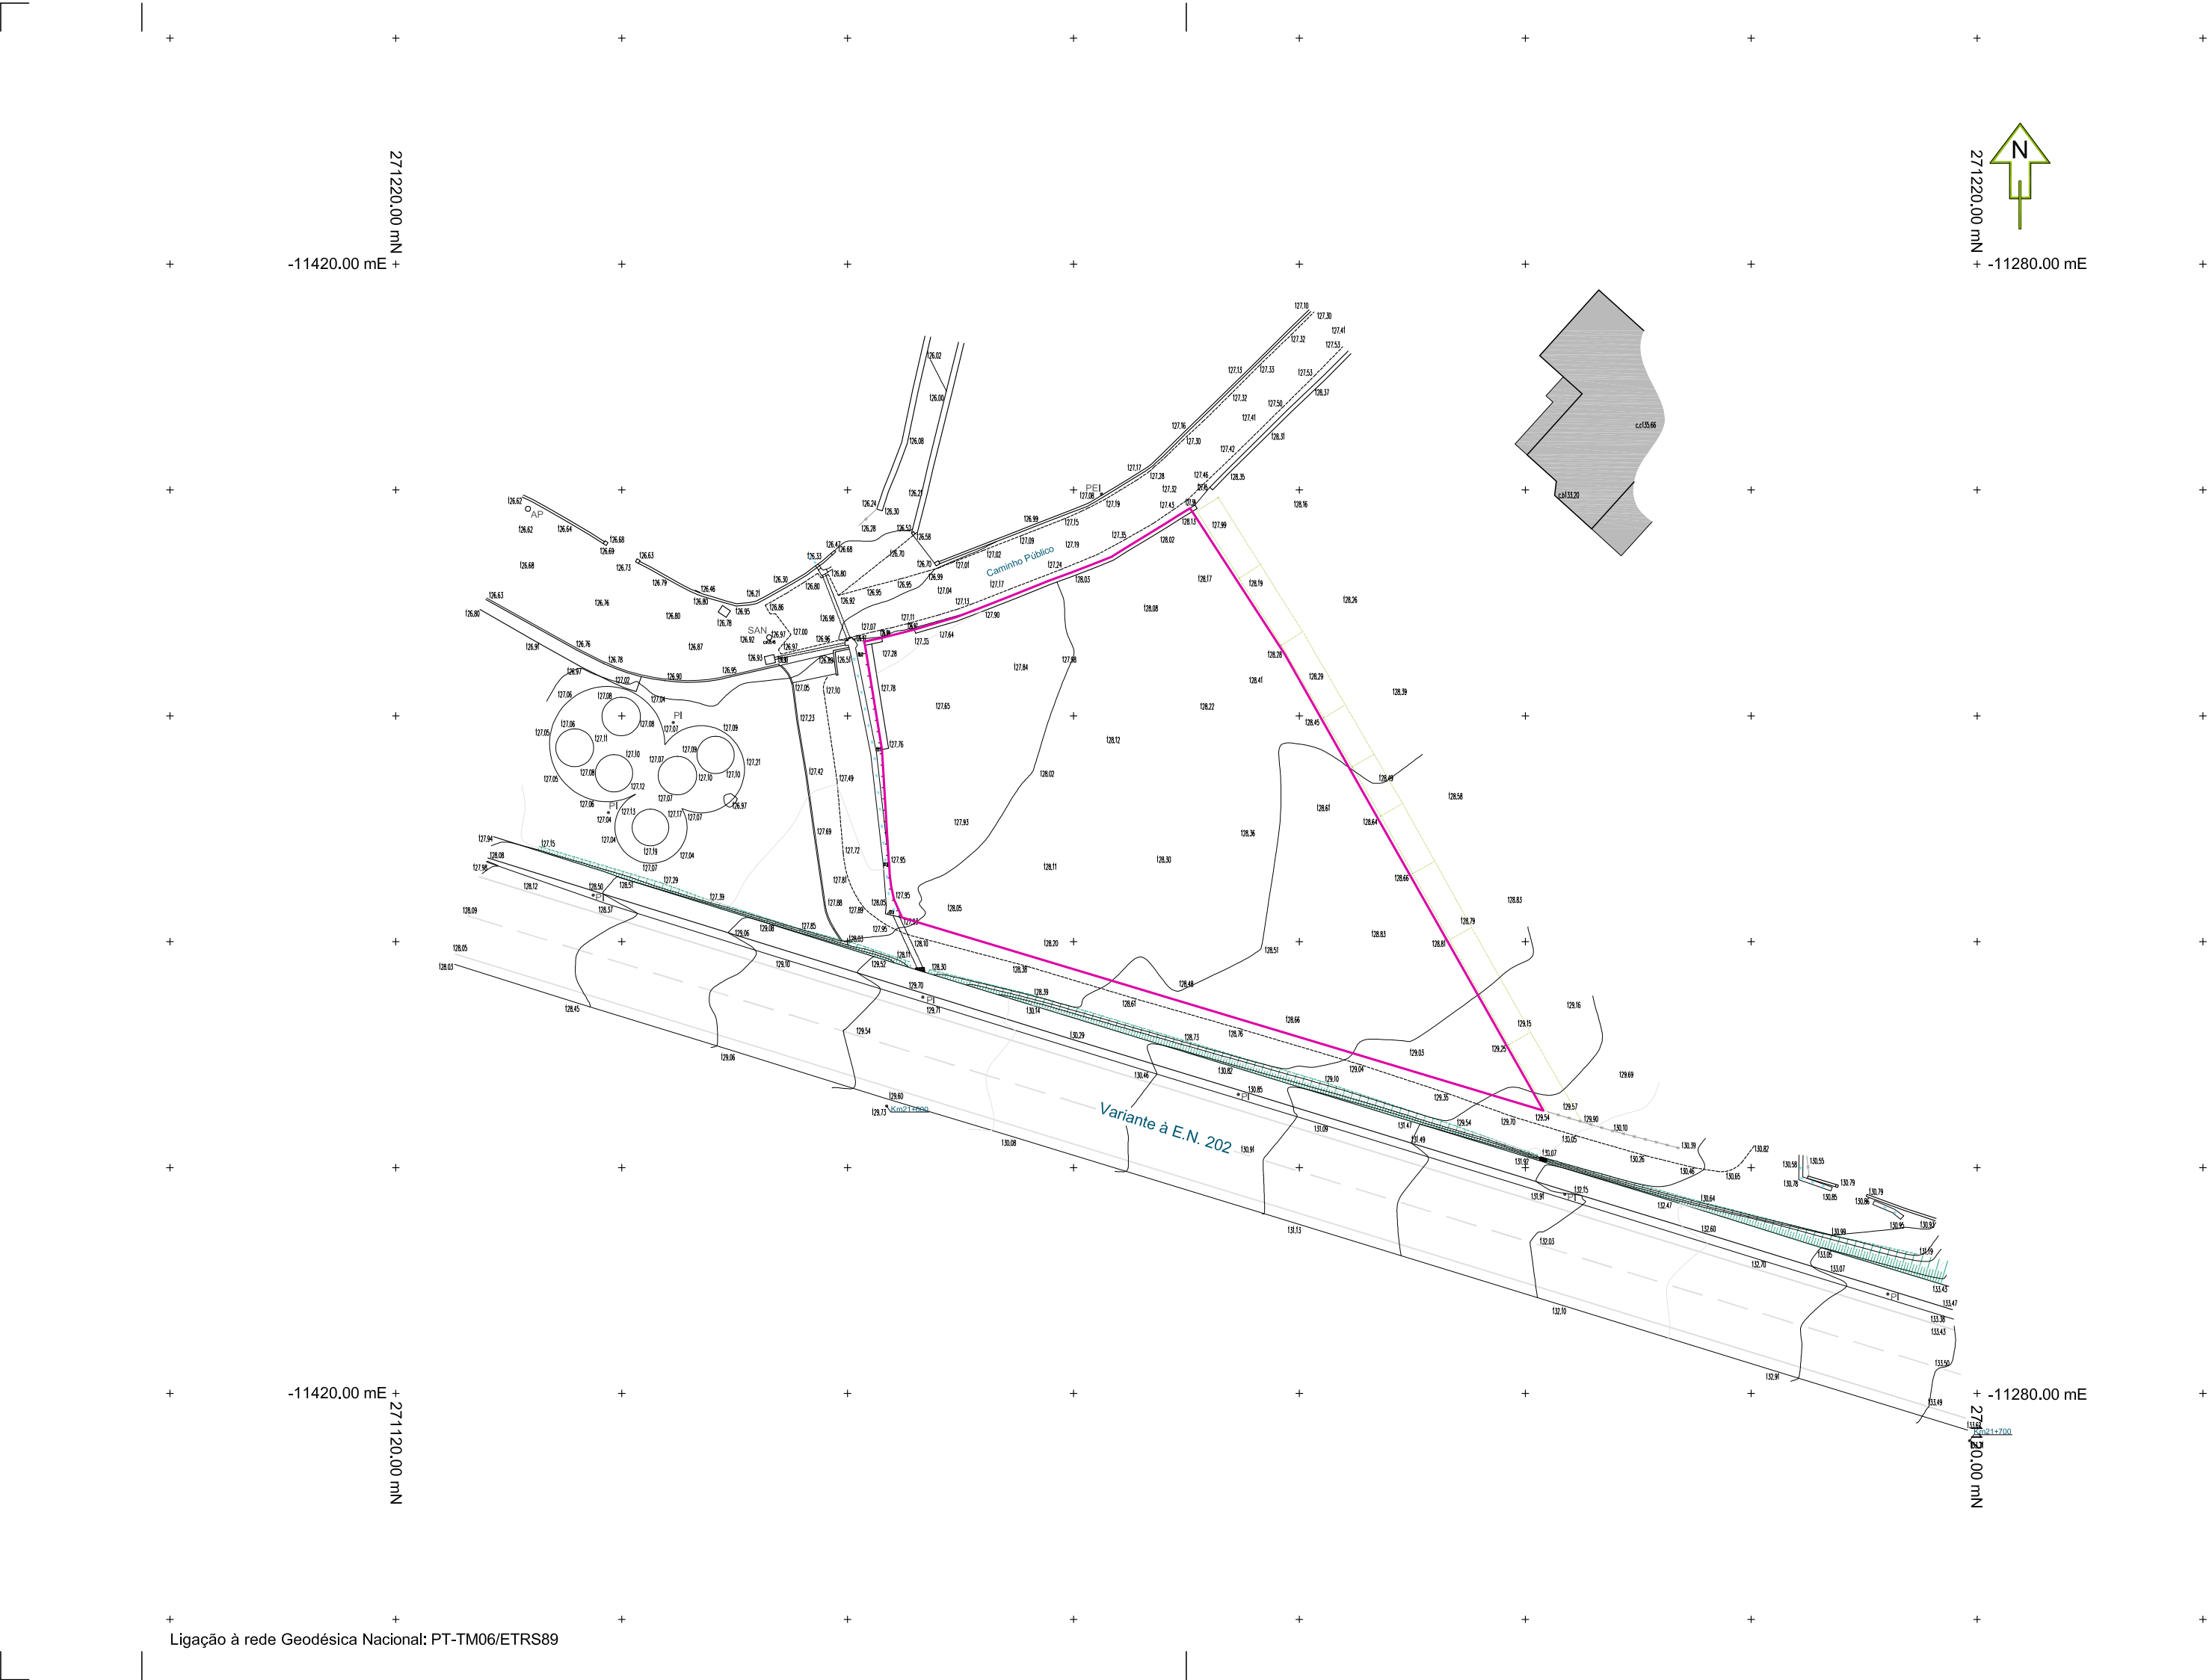

LEGENDA:

Edifício

Anexo

Muro

Muro Suporte

Rede

Talude

Escada

Tanque

49.00

Cota Altimétrica

c.m49.00

Cota Coroamento Muro

c.c49.00

Cota Cumeeira

c.b49.00

Cota Beirao

c.s49.00

Cota Soleira

Deposito

Fossa Séptica

Poço

Poste Telefone

Poste Electrico e Iluminação

Poste Electrico

Poste Iluminação

Águas Pluviais

Saneamento

Válvula Redonda (água)

Válvula Quadrada (água)

Levada

Artº nº -

Área Total: 1614.00m²

Norte: \_\_\_\_\_

Sul: \_\_\_\_\_

Nascente: \_\_\_\_\_

Poente: \_\_\_\_\_

|                                                                         |                                         |           |                                   |   |                      |
|-------------------------------------------------------------------------|-----------------------------------------|-----------|-----------------------------------|---|----------------------|
| <div>ast<sub>lda.</sub></div> <div>ALTITUDE SOLUÇÕES TOPOGRÁFICAS</div> | REQUERENTE: Agência Funerária Mira, Lda |           |                                   |   |                      |
|                                                                         | LOCAL: Galvão - Melgaço                 |           |                                   | 1 |                      |
|                                                                         | PEÇA: Planta Topográfica                |           | ESCALA: 1/500                     |   |                      |
|                                                                         | DATA: JUN.2020                          | T-4277-20 | LEVANTOU: M.BAGANHA<br>J.VALINHAS |   | VERIFICOU: M.BAGANHA |
|                                                                         |                                         |           | DESENHOU: M.BAGANHA               |   | APROVOU: M.BAGANHA   |